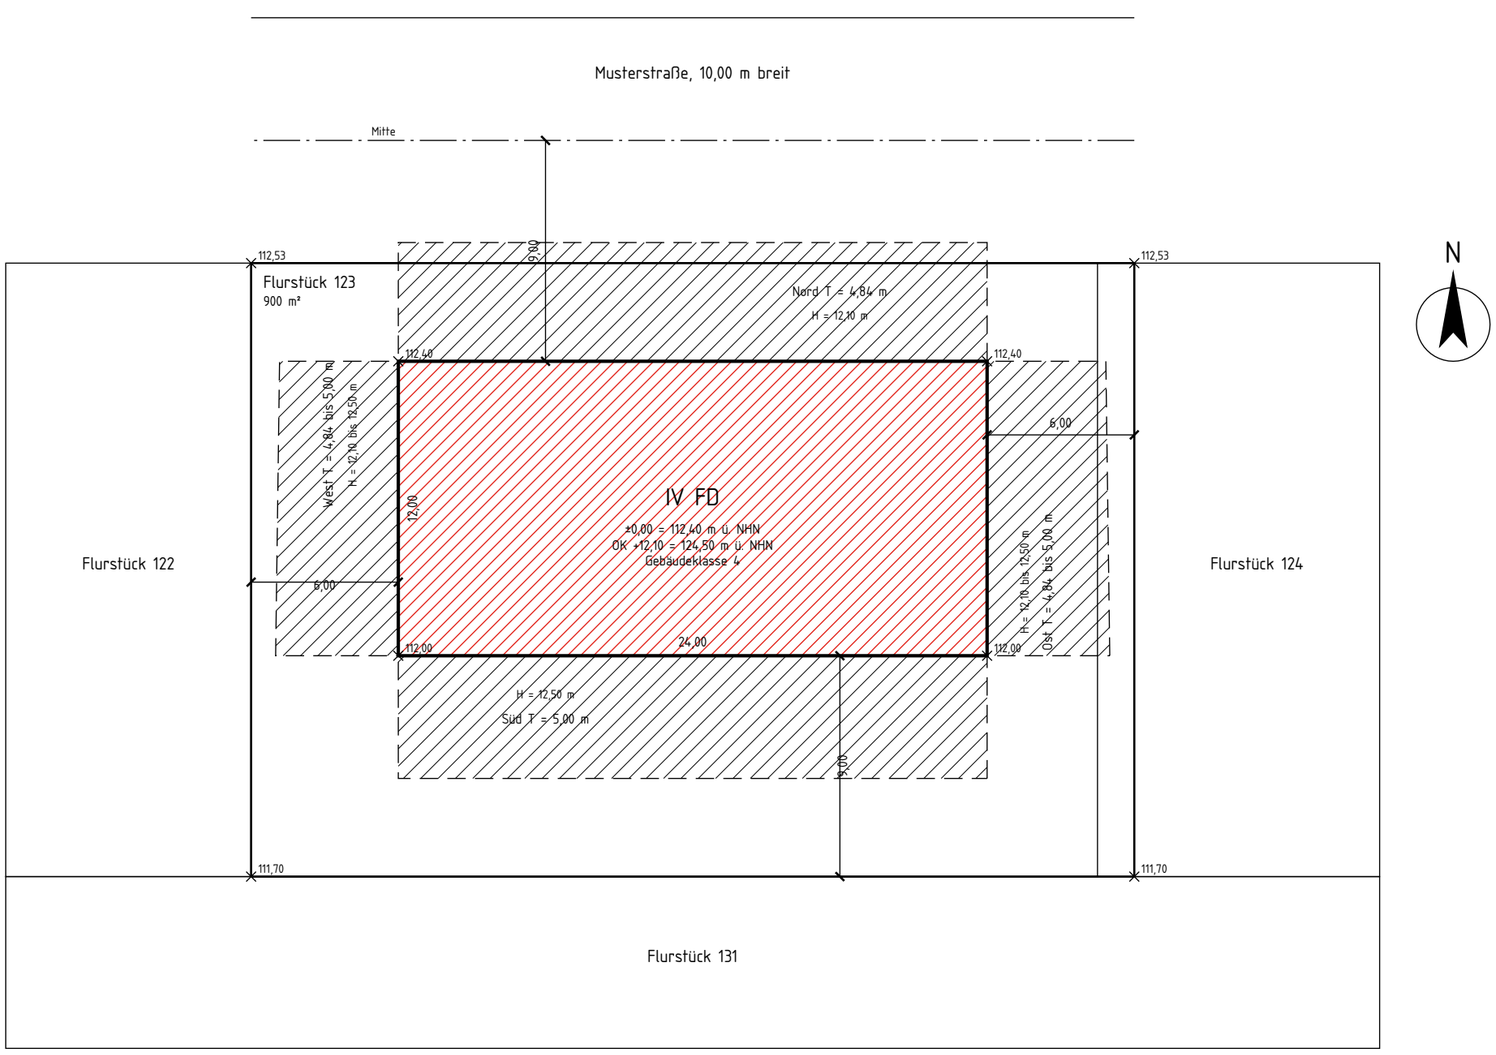


Abstandsflächen nach § 6 MBO (Musterbauordnung (MBO 2002)): T = 0,4 H, mindestens 3,00 m
Alle Abstandsflächen liegen auf dem Grundstück oder bis zur Mitte öffentlicher Flächen

Lageplan

M 1:250

Bauvorhaben

Neubau eines Mehrfamilienhauses mit 8 Wohnungen


Bauherr	Bauort, Grundstück	Entwurfsverfasser
Wohnbau Muster GmbH (Testdaten)	Musterstraße 12, 12345 Musterstadt Gemarkung Musterstadt, Flur 3, Flurstück 123	Lot Testbüro (Testdaten) Beispielweg 5, 12345 Musterstadt Architektenkammer Nr. 00000

Planinhalt

Lageplan mit Abstandsflächen

Maßstab	Format	Datum	Index	Plan-Nr.
1:250	A3	24.10.2026		BA-01

Bauherr: Datum, Unterschrift	Entwurfsverfasser: Datum, Unterschrift

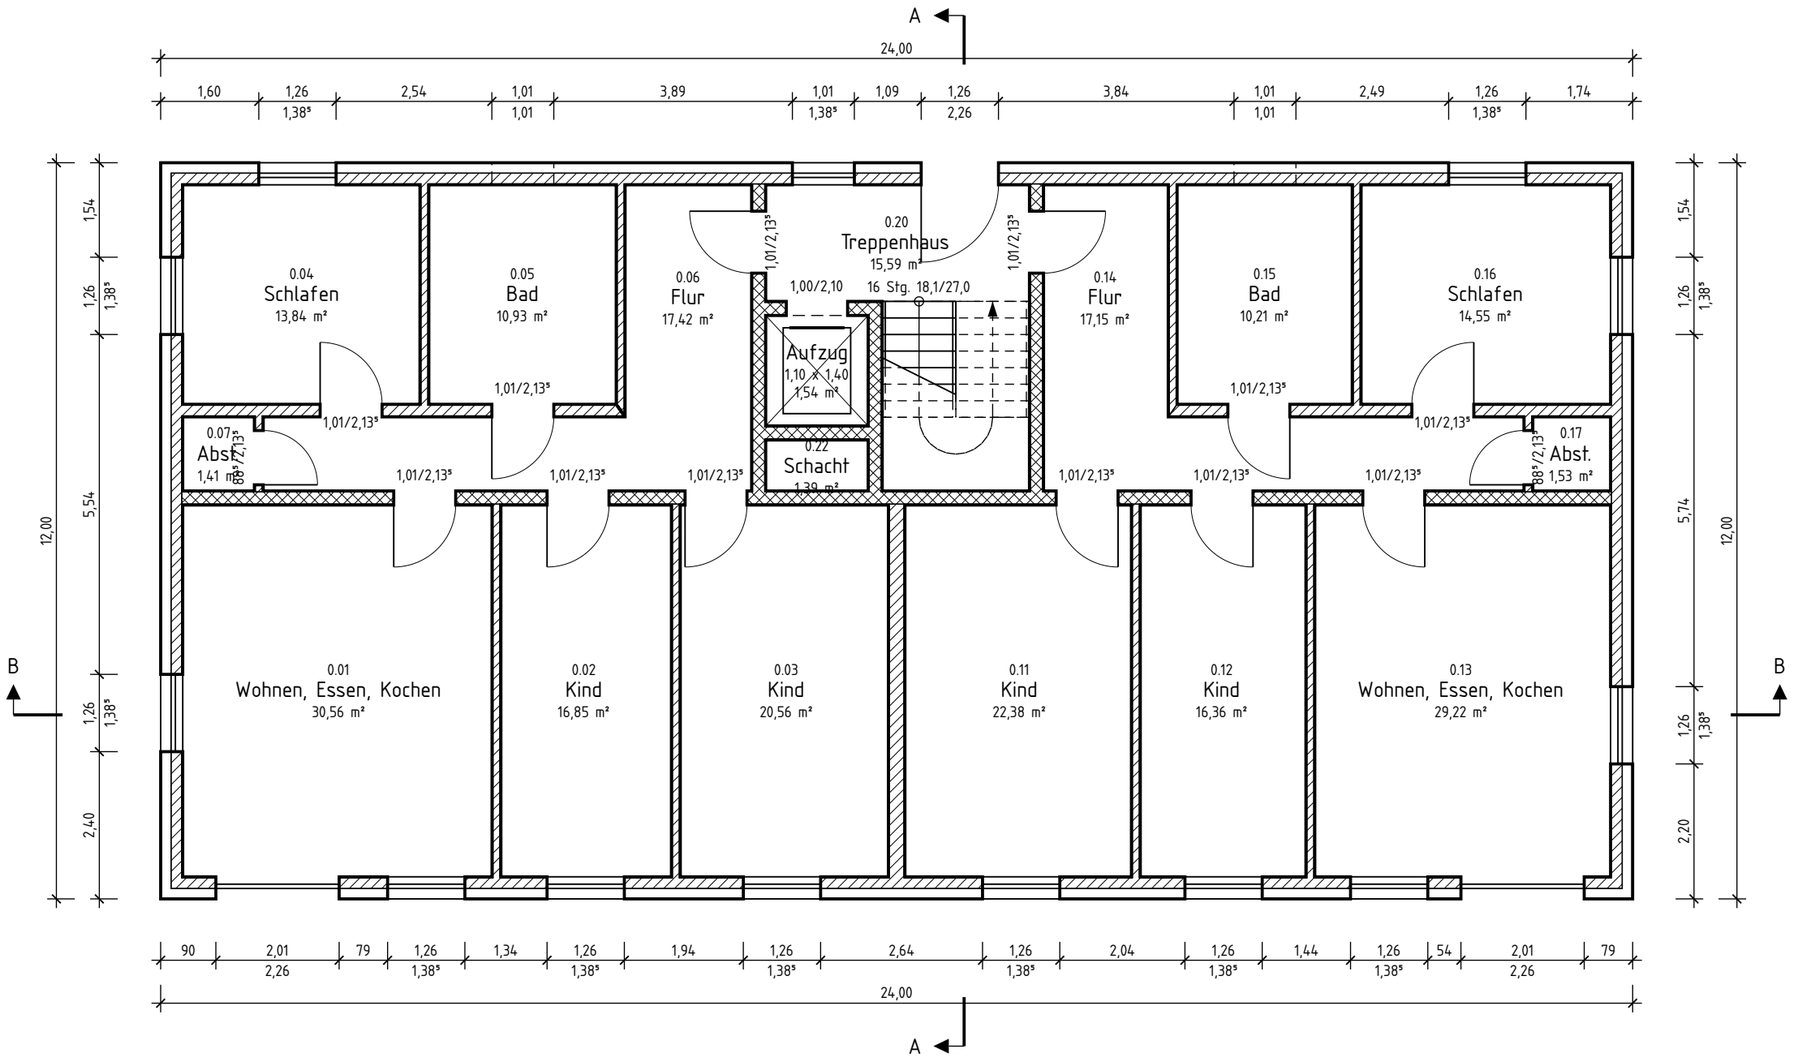

Grundriss EG

M 1:100

Bauvorhaben

Neubau eines Mehrfamilienhauses mit 8 Wohnungen


Bauherr	Bauort, Grundstück	Entwurfsverfasser
Wohnbau Muster GmbH (Testdaten)	Musterstraße 12, 12345 Musterstadt Gemarkung Musterstadt, Flur 3, Flurstück 123	Lot Testbüro (Testdaten) Beispielweg 5, 12345 Musterstadt Architektenkammer Nr. 00000

Planinhalt

Grundriss Erdgeschoss

Maßstab	Format	Datum	Index	Plan-Nr.
1:100	A3	24.10.2026		BA-02

Bauherr: Datum, Unterschrift	Entwurfsverfasser: Datum, Unterschrift

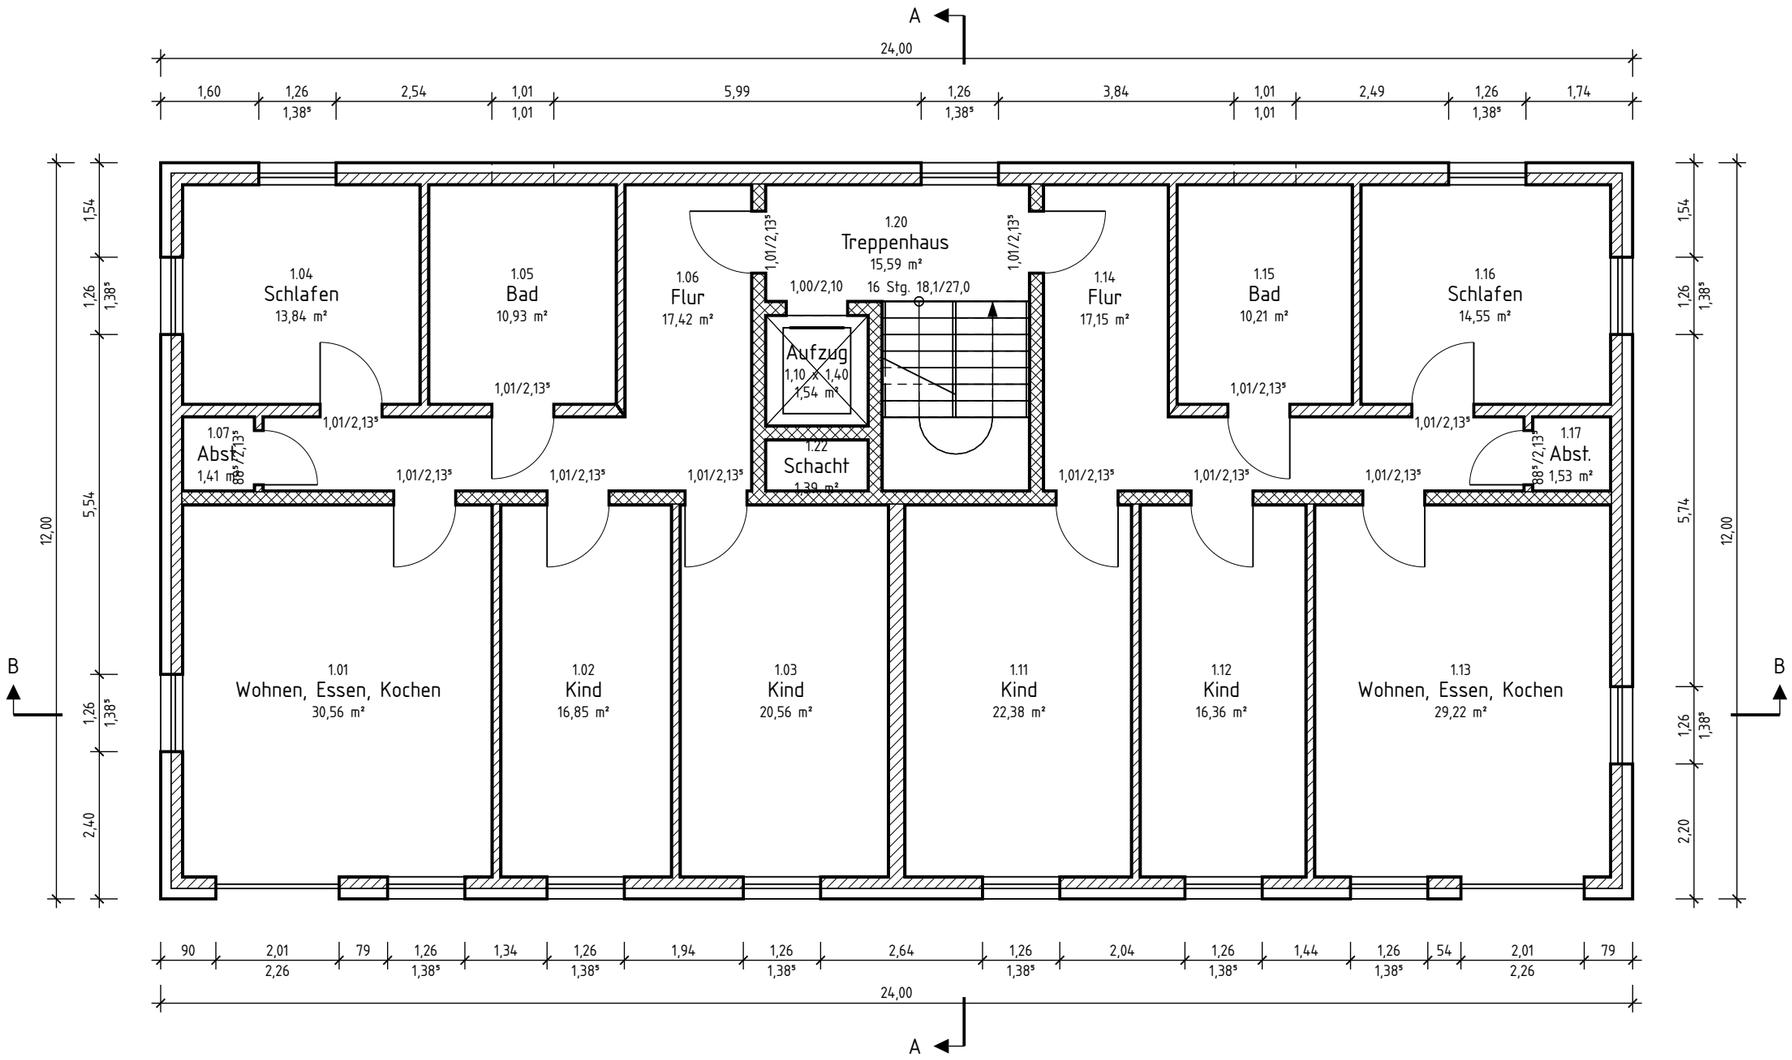

Grundriss 1.OG

M 1:100

Bauvorhaben

Neubau eines Mehrfamilienhauses mit 8 Wohnungen


Bauherr	Bauort, Grundstück	Entwurfsverfasser
Wohnbau Muster GmbH (Testdaten)	Musterstraße 12, 12345 Musterstadt Gemarkung Musterstadt, Flur 3, Flurstück 123	Lot Testbüro (Testdaten) Beispielweg 5, 12345 Musterstadt Architektenkammer Nr. 00000

Planinhalt

Grundriss 1. Obergeschoss

Maßstab	Format	Datum	Index	Plan-Nr.
1:100	A3	24.10.2026		BA-03


Bauherr: Datum, Unterschrift	Entwurfsverfasser: Datum, Unterschrift

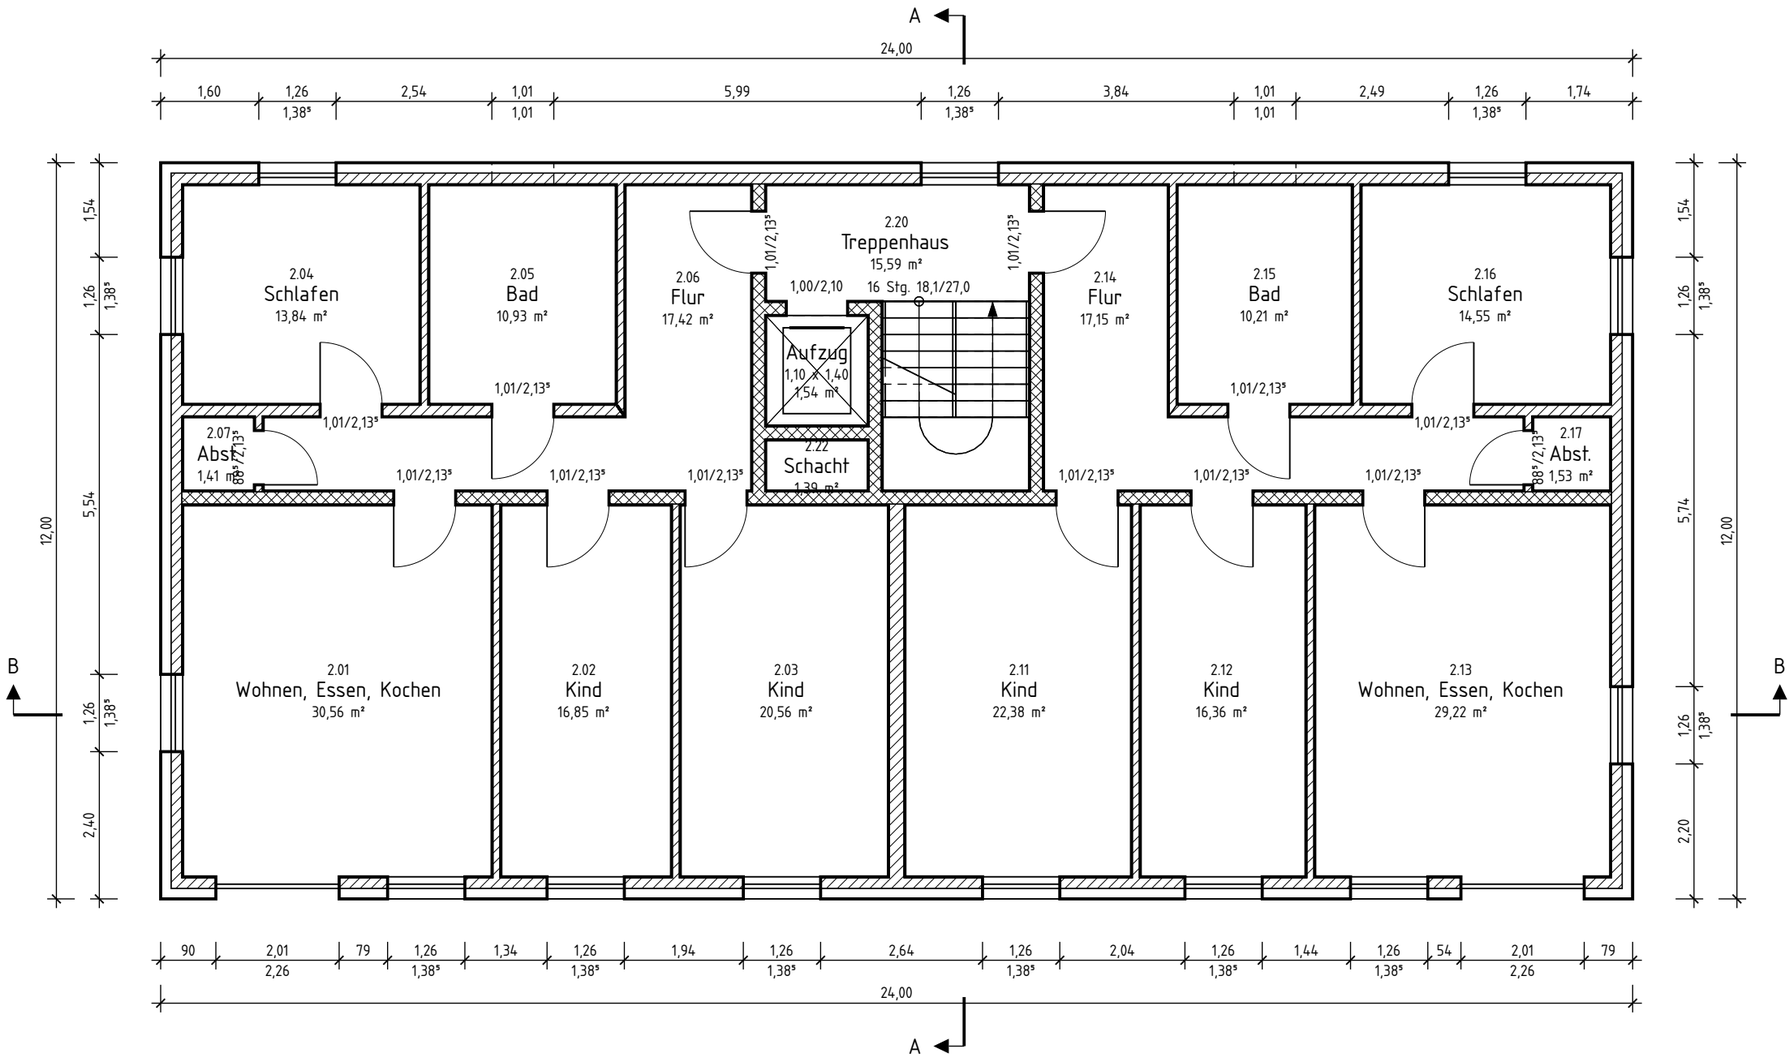

Grundriss 2.OG

M 1:100

Bauvorhaben: Neubau eines Mehrfamilienhauses mit 8 Wohnungen				
Bauherr: Wohnbau Muster GmbH (Testdaten)	Bauort, Grundstück: Musterstraße 12, 12345 Musterstadt Gemarkung Musterstadt, Flur 3, Flurstück 123	Entwurfsverfasser: Lot Testbüro (Testdaten) Beispielweg 5, 12345 Musterstadt Architektenkammer Nr. 00000		
Planinhalt: Grundriss 2. Obergeschoss				
Maßstab: 1:100	Format: A3	Datum: 24.10.2026	Index:	Plan-Nr.: BA-04
Bauherr: Datum, Unterschrift		Entwurfsverfasser: Datum, Unterschrift		

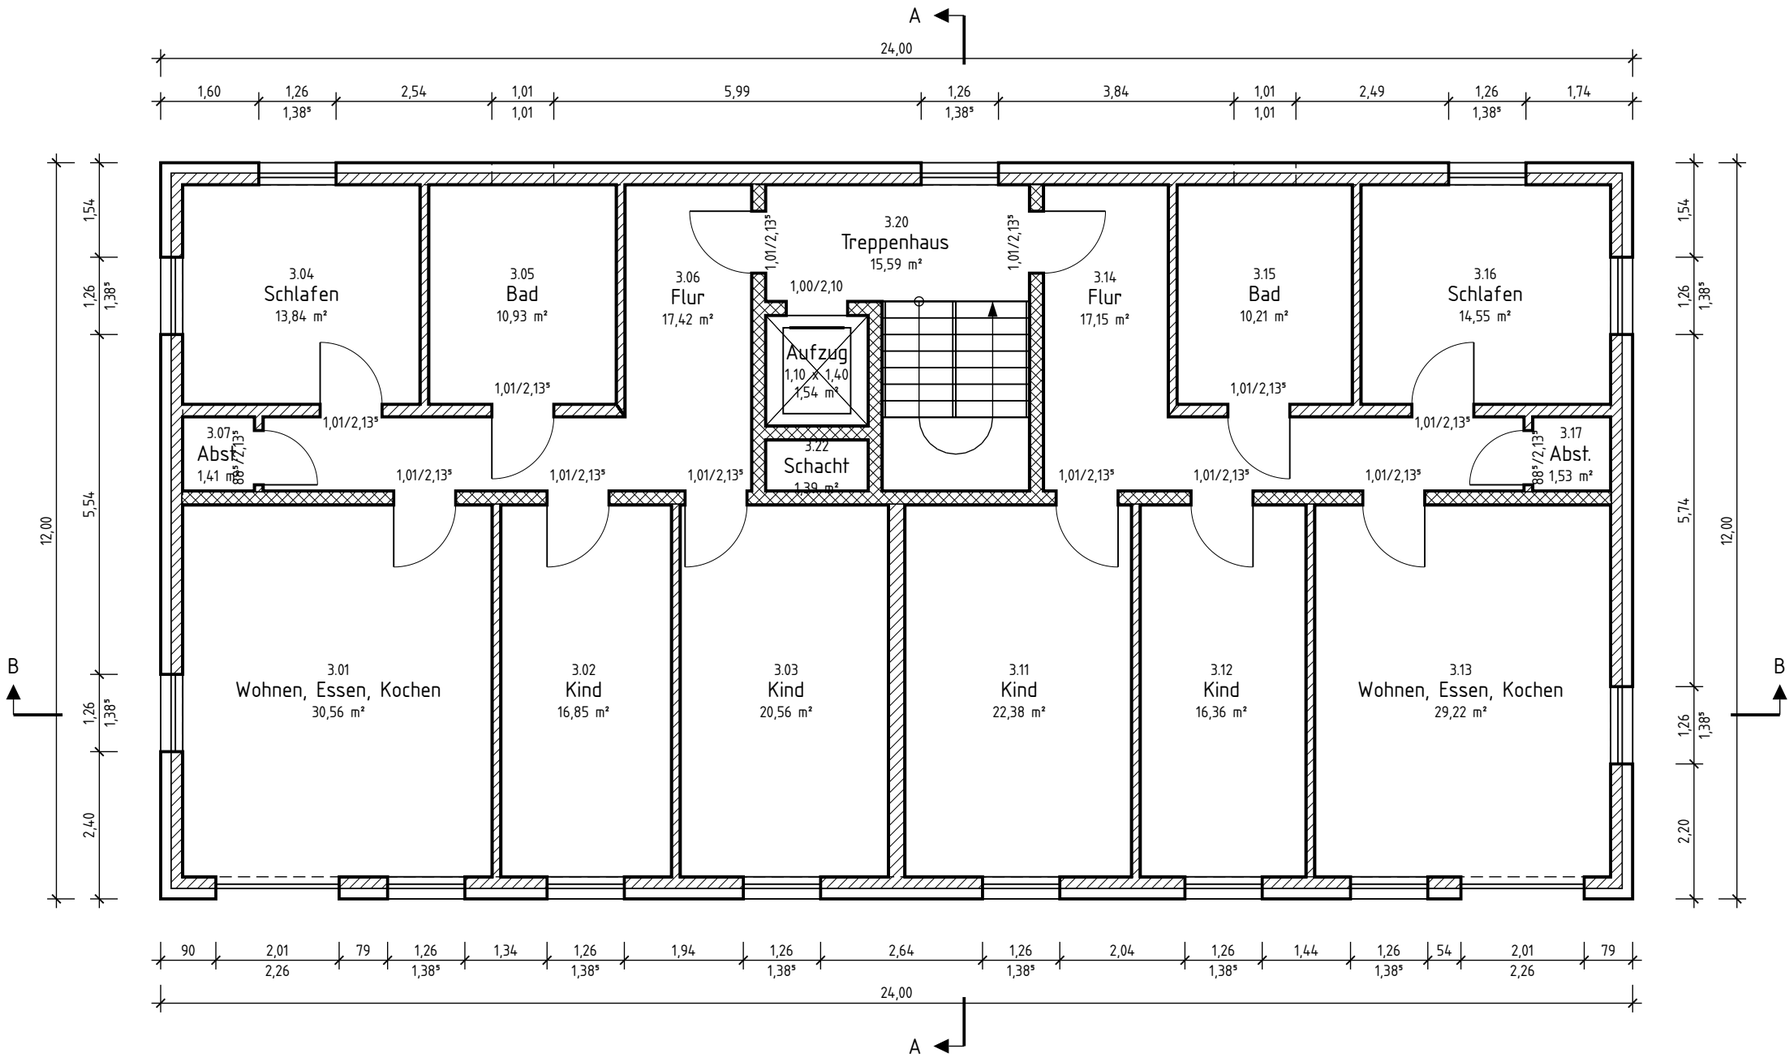

Grundriss 3.OG

M 1:100

Bauvorhaben

Neubau eines Mehrfamilienhauses mit 8 Wohnungen


Bauherr	Bauort, Grundstück	Entwurfsverfasser
Wohnbau Muster GmbH (Testdaten)	Musterstraße 12, 12345 Musterstadt Gemarkung Musterstadt, Flur 3, Flurstück 123	Lot Testbüro (Testdaten) Beispielweg 5, 12345 Musterstadt Architektenkammer Nr. 00000

Planinhalt

Grundriss 3. Obergeschoss


Maßstab	Format	Datum	Index	Plan-Nr.
1:100	A3	24.10.2026		BA-05

Bauherr: Datum, Unterschrift	Entwurfsverfasser: Datum, Unterschrift

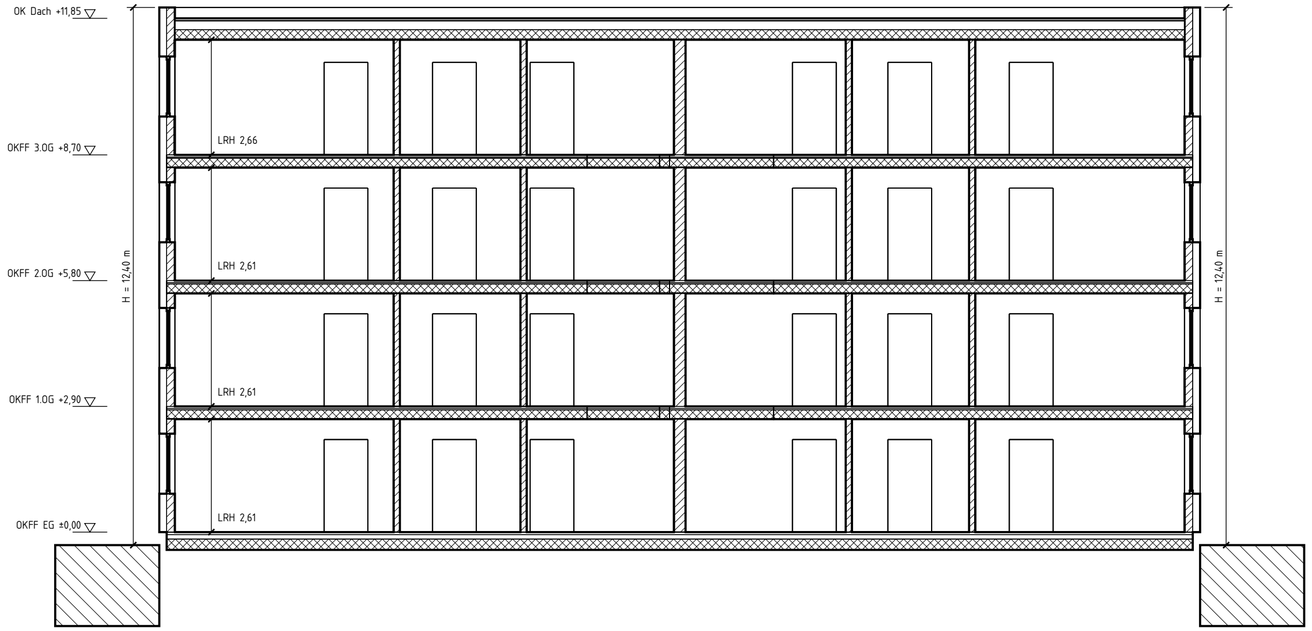

Schnitt B-B

M 1:100

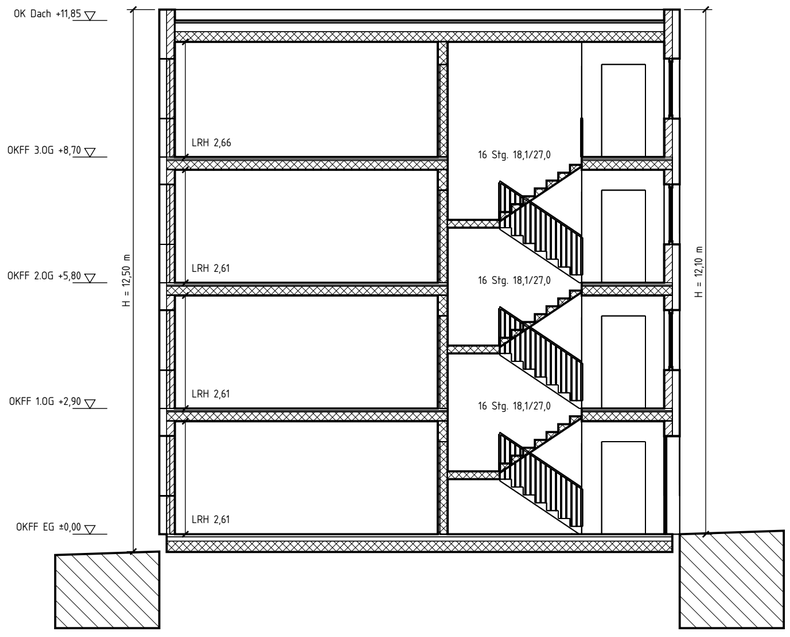

Schnitt A-A

M 1:100

Bauvorhaben

Neubau eines Mehrfamilienhauses mit 8 Wohnungen


Bauherr	Bauort, Grundstück	Entwurfsverfasser
Wohnbau Muster GmbH (Testdaten)	Musterstraße 12, 12345 Musterstadt Gemarkung Musterstadt, Flur 3, Flurstück 123	Lot Testbüro (Testdaten) Beispielweg 5, 12345 Musterstadt Architektenkammer Nr. 00000

Planinhalt

Schnitte


Maßstab	Format	Datum	Index	Plan-Nr.
1:100	A2	24.10.2026		BA-06

Bauherr: Datum, Unterschrift	Entwurfsverfasser: Datum, Unterschrift

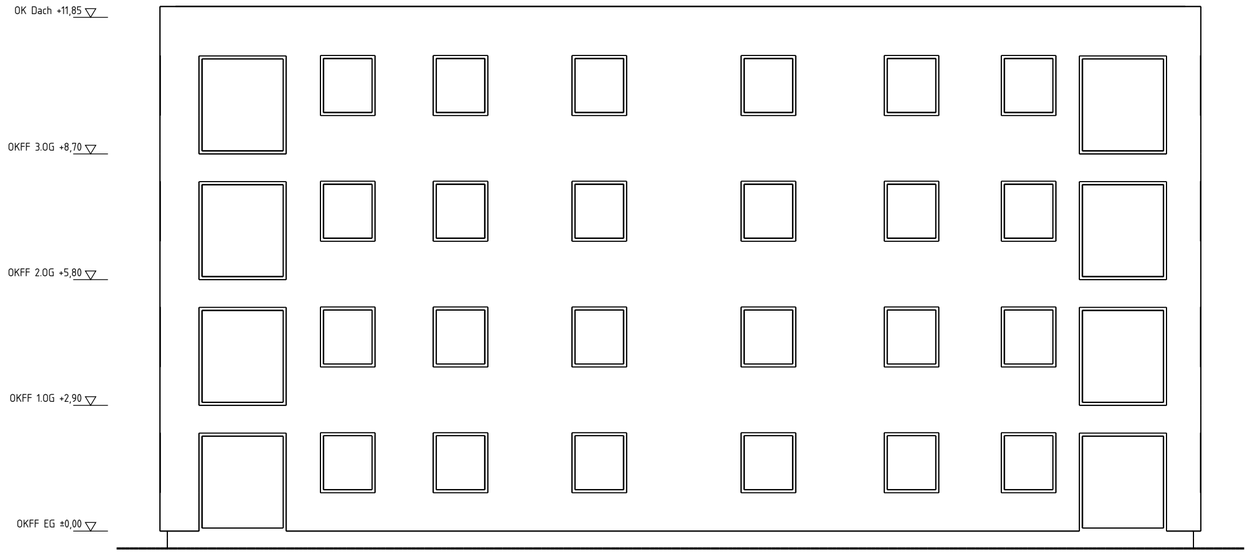

Ansicht Süd

M 1:100

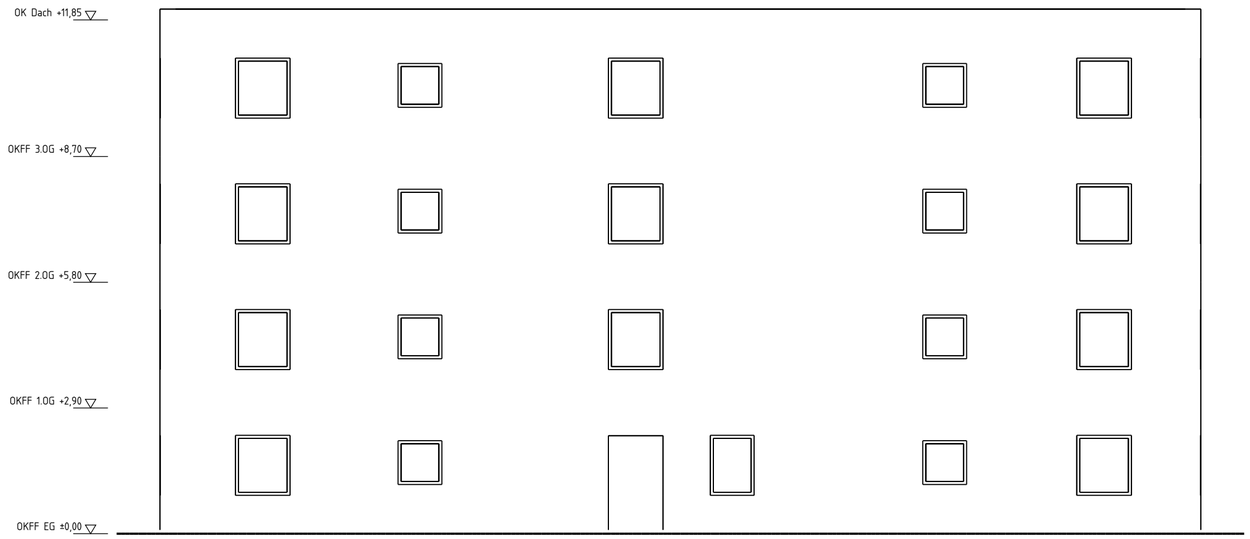

Ansicht Nord

M 1:100

Bauvorhaben

Neubau eines Mehrfamilienhauses mit 8 Wohnungen


Bauherr	Bauort, Grundstück	Entwurfsverfasser
Wohnbau Muster GmbH (Testdaten)	Musterstraße 12, 12345 Musterstadt Gemarkung Musterstadt, Flur 3, Flurstück 123	Lot Testbüro (Testdaten) Beispielweg 5, 12345 Musterstadt Architektenkammer Nr. 00000

Planinhalt

Ansichten Süd und Nord


Maßstab	Format	Datum	Index	Plan-Nr.
1:100	A2	24.10.2026		BA-07

Bauherr: Datum, Unterschrift	Entwurfsverfasser: Datum, Unterschrift

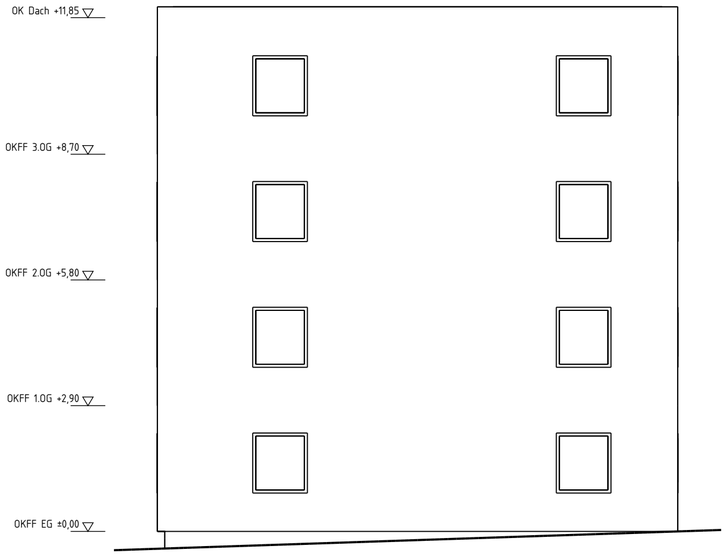

Ansicht Ost

M 1:100

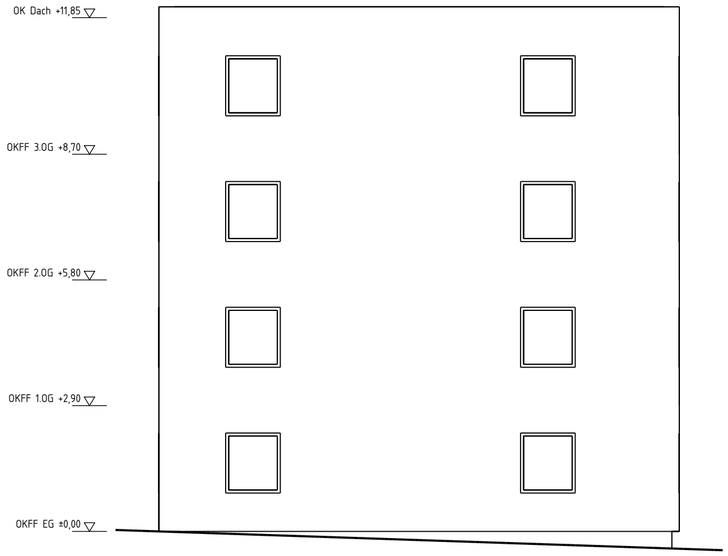

Ansicht West

M 1:100

Bauvorhaben

Neubau eines Mehrfamilienhauses mit 8 Wohnungen


Bauherr	Bauort, Grundstück	Entwurfsverfasser
Wohnbau Muster GmbH (Testdaten)	Musterstraße 12, 12345 Musterstadt Gemarkung Musterstadt, Flur 3, Flurstück 123	Lot Testbüro (Testdaten) Beispielweg 5, 12345 Musterstadt Architektenkammer Nr. 00000

Planinhalt

Ansichten Ost und West


Maßstab	Format	Datum	Index	Plan-Nr.
1:100	A2	24.10.2026		BA-08

Bauherr: Datum, Unterschrift	Entwurfsverfasser: Datum, Unterschrift

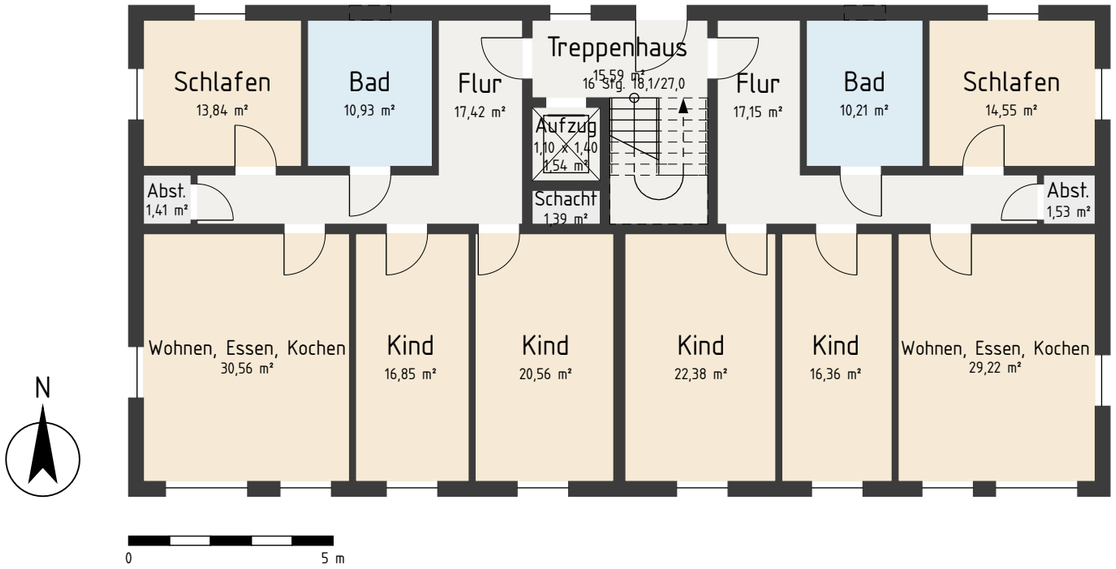

Grundriss EG

M 1:150

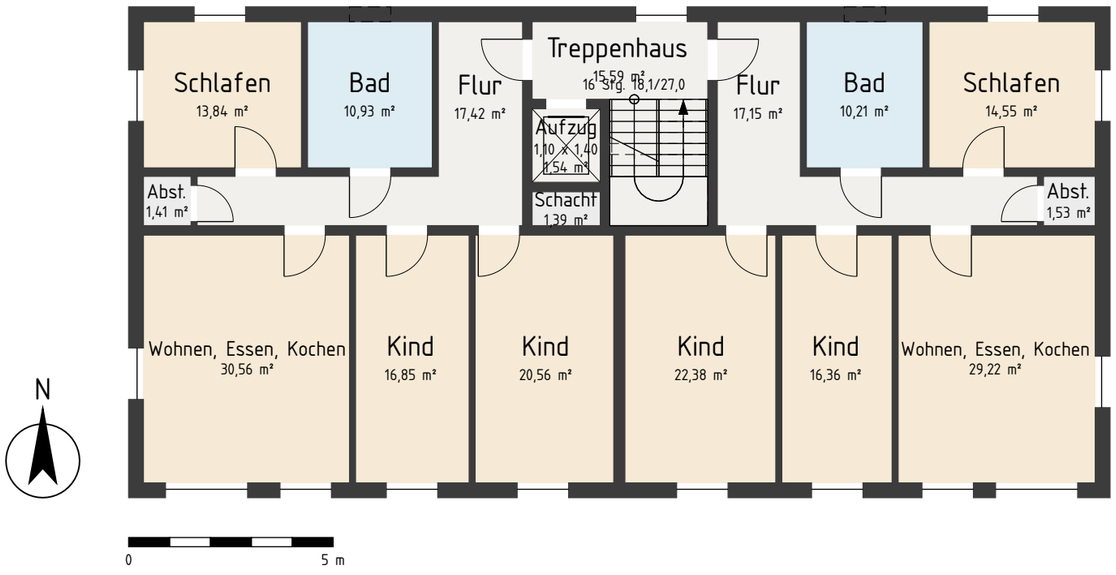

Grundriss 1.OG

M 1:150

Bauvorhaben

Neubau eines Mehrfamilienhauses mit 8 Wohnungen

Bauherr	Bauort, Grundstück	Entwurfsverfasser
Wohnbau Muster GmbH (Testdaten)	Musterstraße 12, 12345 Musterstadt Gemarkung Musterstadt, Flur 3, Flurstück 123	Lot Testbüro (Testdaten) Beispielweg 5, 12345 Musterstadt Architektenkammer Nr. 00000

Planinhalt

Präsentation Erdgeschoss und Regelgeschoss

Maßstab	Format	Datum	Index	Plan-Nr.
1:150	A3	24.10.2026		P-01

Bauherr: Datum, Unterschrift	Entwurfsverfasser: Datum, Unterschrift