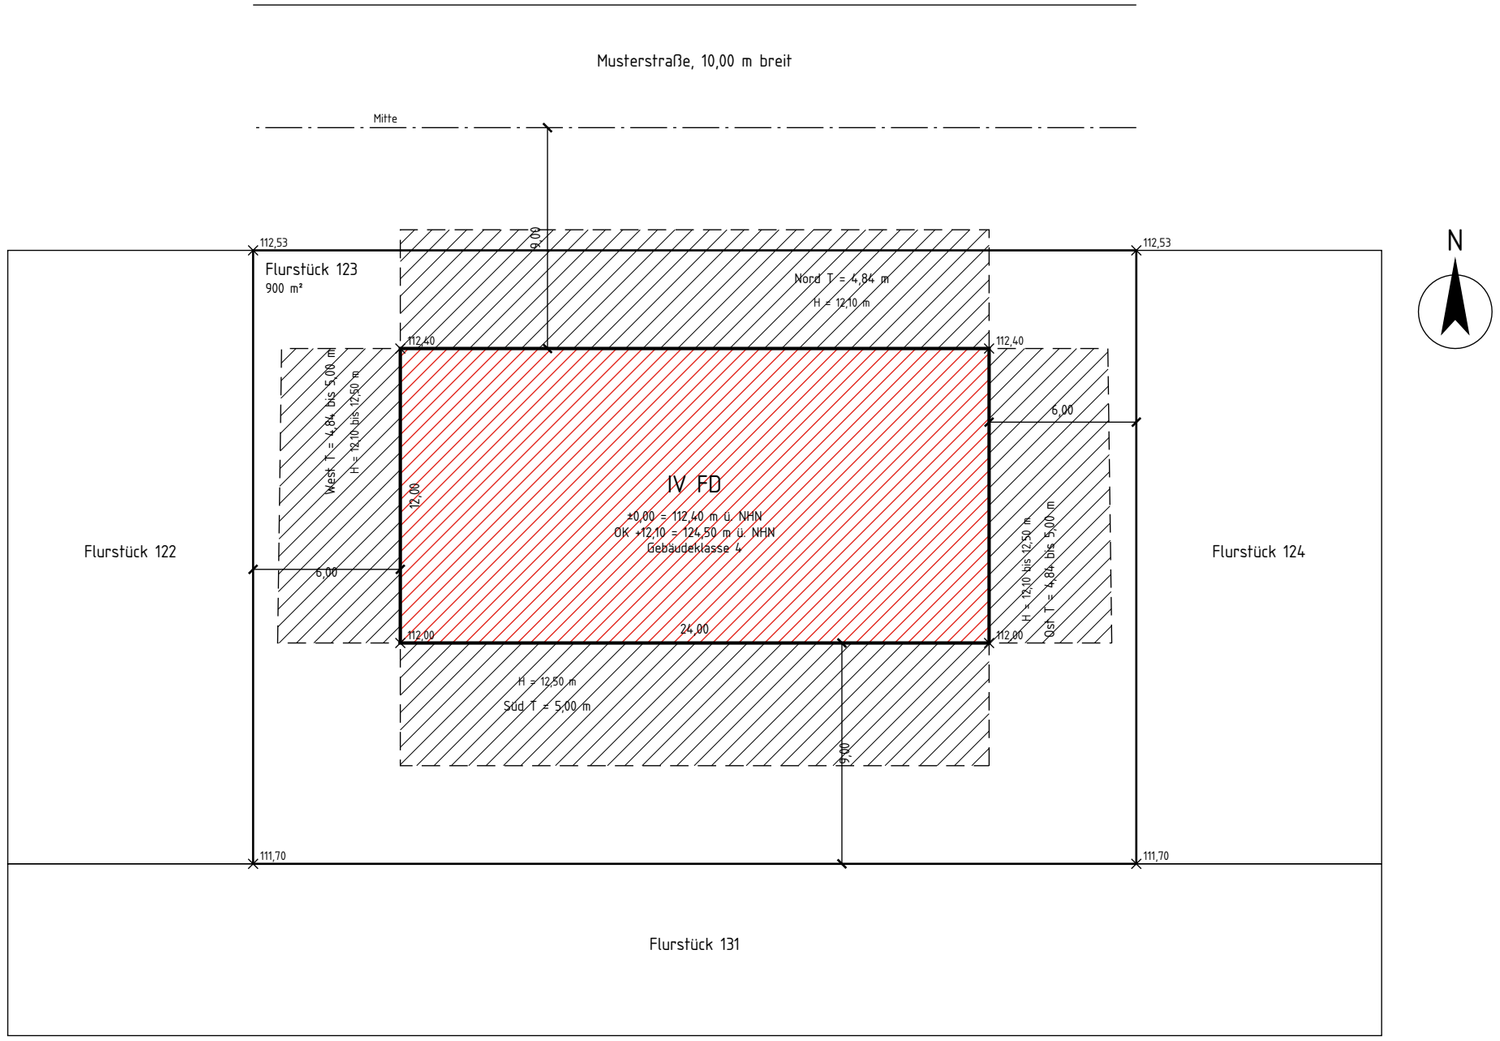

Abstandsflächen nach § 6 MBO (Musterbauordnung (MBO 2002)): T = 0,4 H, mindestens 3,00 m
Alle Abstandsflächen liegen auf dem Grundstück oder bis zur Mitte öffentlicher Flächen

MFH Testprojekt · Lageplan mit Abstandsflächen · M 1:250

Abstandsflächen eingehalten. Gebäudeklasse nach § 2 Abs. 3 MBO. Darstellung nach Bürostandard, Vorschlag.